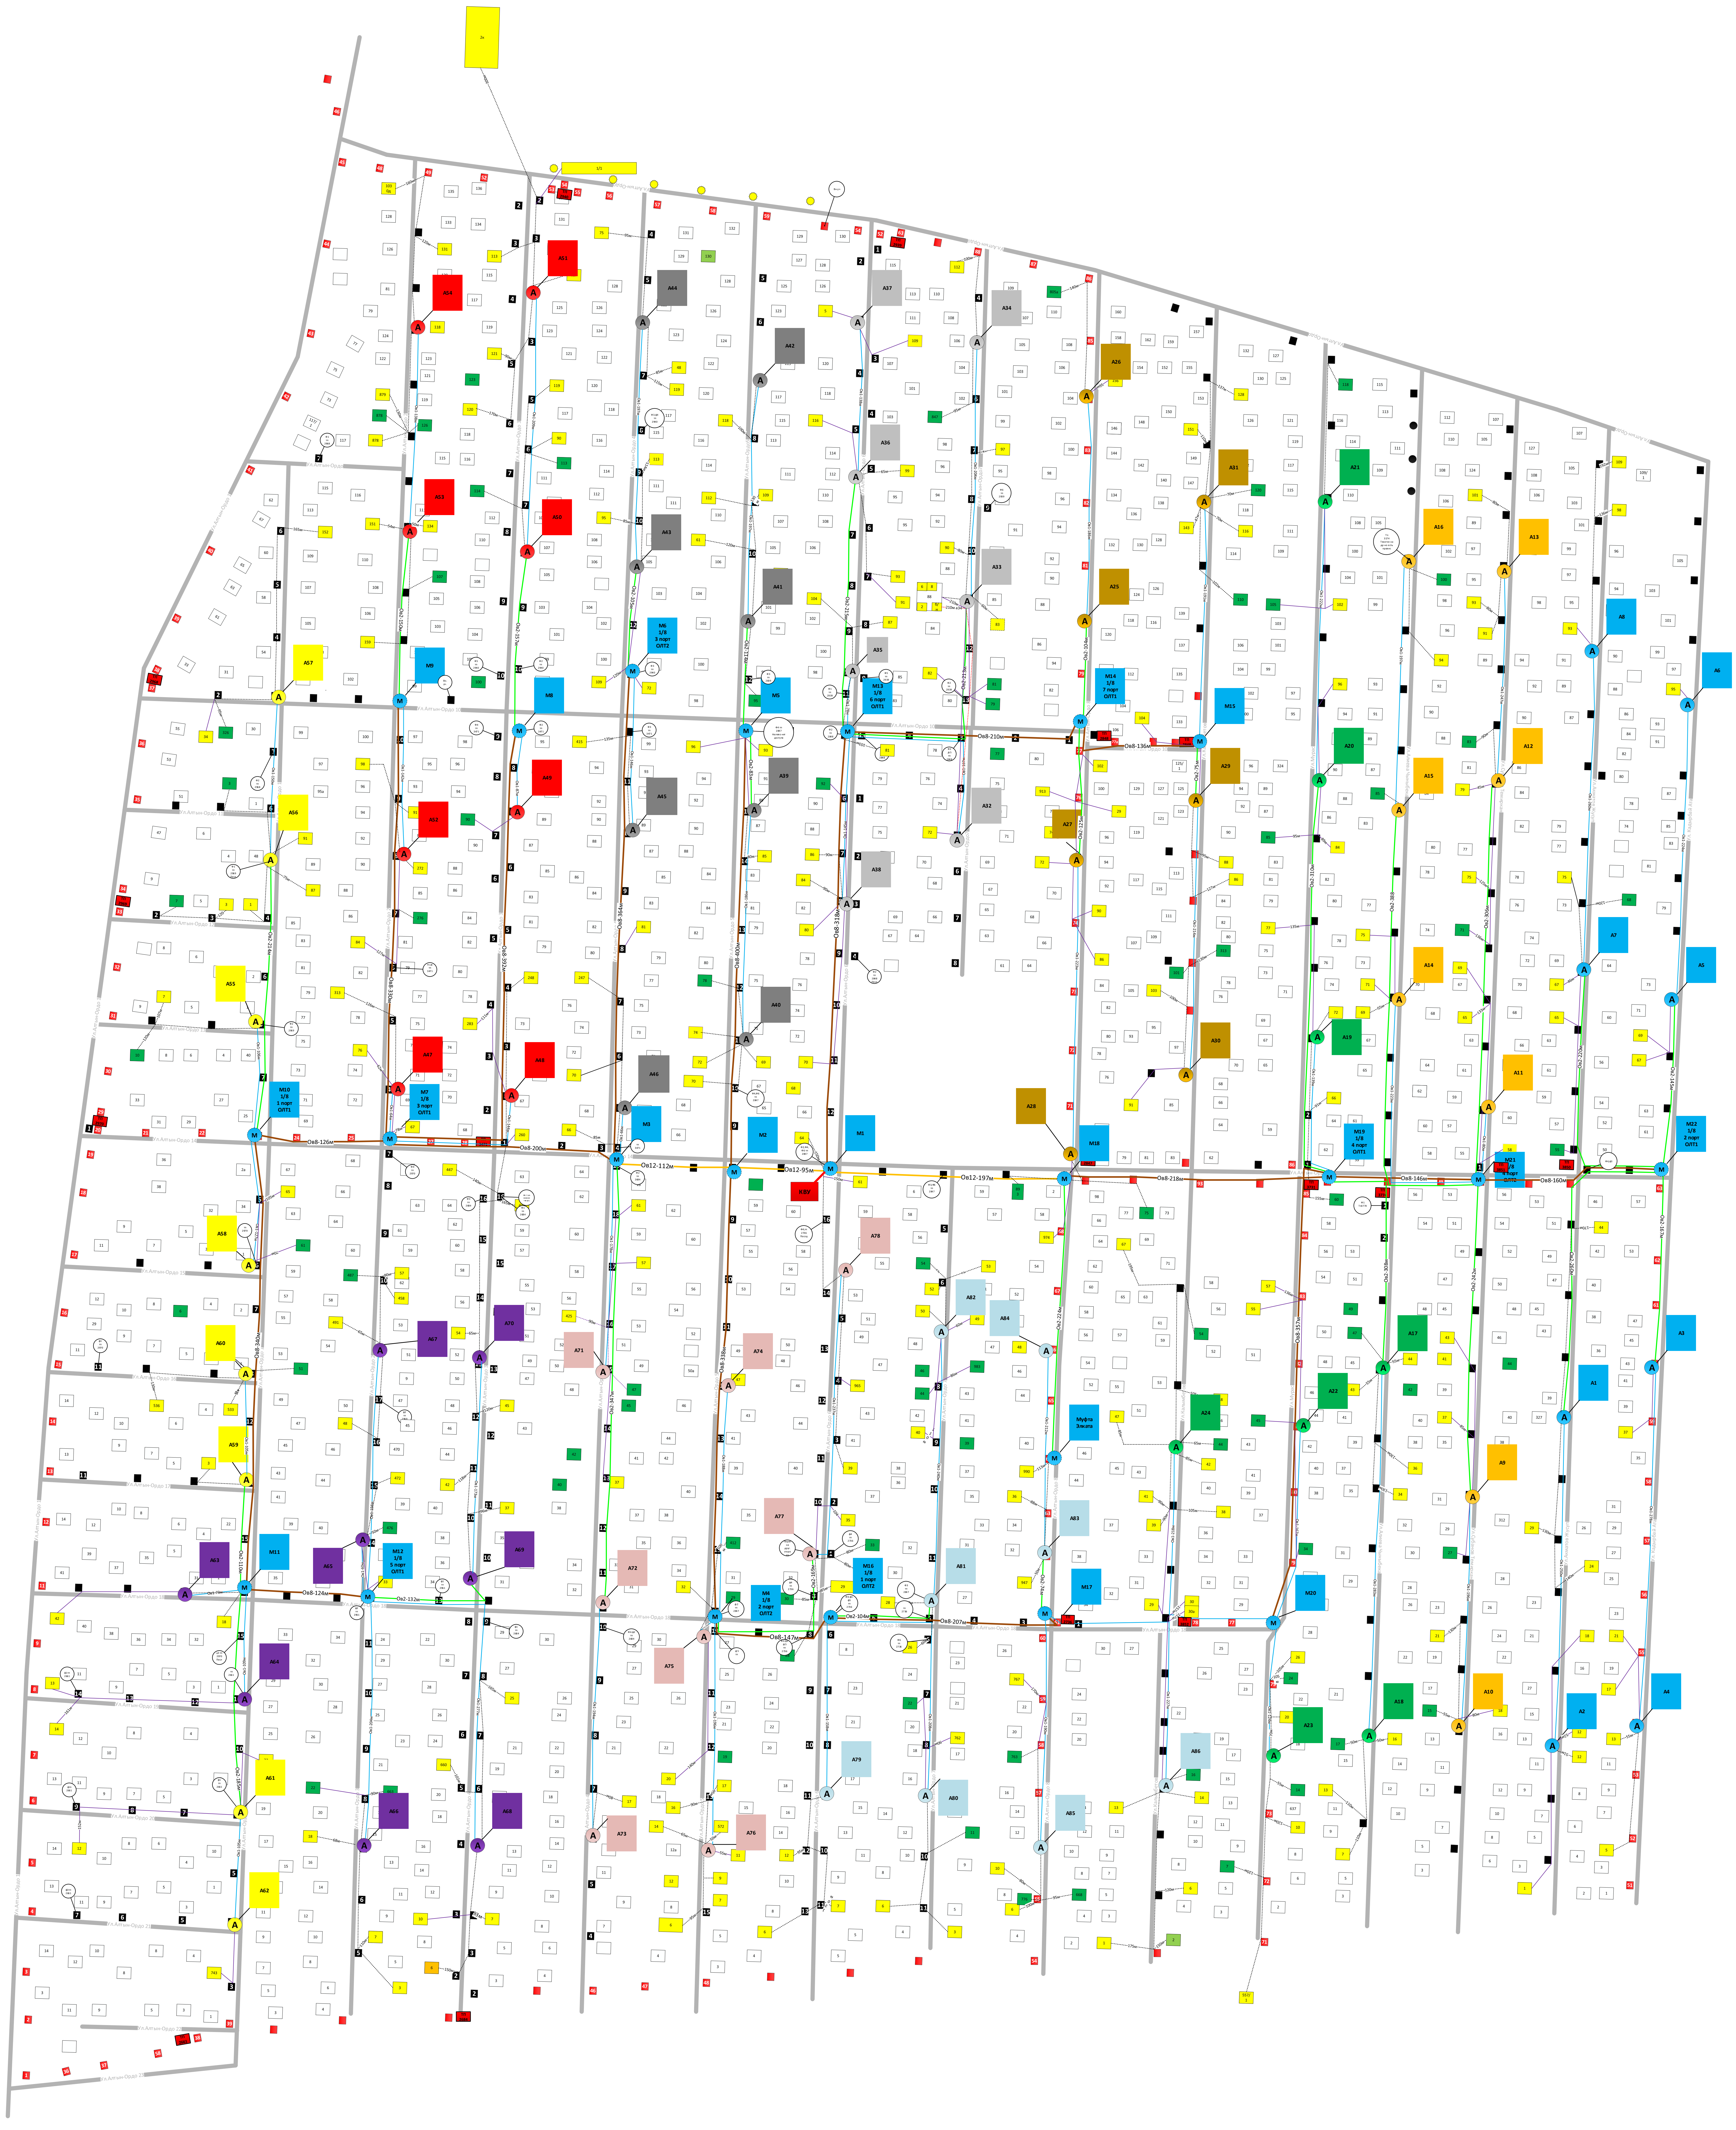
2к
1/1
Вкл
Ул.Алтын-Ордо
Ул.Алтын-Ордо 1
Ул.Алтын-Ордо 2
Ул.Алтын-Ордо 3
Ул.Алтын-Ордо 4
Ул.Алтын-Ордо 5
Ул.Алтын-Ордо 6
Ул.Алтын-Ордо 7
Ул.Алтын-Ордо 8
Ул.Алтын-Ордо 10
Ул.Алтын-Ордо 11
Ул.Алтын-Ордо 12
Ул.Алтын-Ордо 13
Ул.Алтын-Ордо 14
Ул.Алтын-Ордо 15
Ул.Алтын-Ордо 16
Ул.Алтын-Ордо 17
Ул.Алтын-Ордо 18
Ул.Алтын-Ордо 19
Ул.Алтын-Ордо 20
Ул.Алтын-Ордо 21
Ул.Алтын-Ордо 22
Ул.Алтын-Ордо 23
Ул.Мурас
Ул.Алиева Чыныбека
Ул.Субанов Темиркан
Ул.Акматов Жусуп
Ул.Кадырбай Ата
Ул.Калымбетов
ТП 2946
ТП 2939
ТП 2968
ТП 2969
ТП 2970
ТП 2848
ТП 3731
ТП 3851
ТП 3450
ТП 2736
ТП 2857
ТП 2684
ТП 2661
ТП 3174 Тянется на др но есть провис
М1
М2
М3
М4 1/8 2 порт ОЛТ2
М5
М6 1/8 3 порт ОЛТ2
М7 1/8 3 порт ОЛТ1
М8
М9
М10 1/8 1 порт ОЛТ1
М11
М12 1/8 5 порт ОЛТ1
М13 1/8 6 порт ОЛТ1
М14 1/8 7 порт ОЛТ1
М15
М16 1/8 1 порт ОЛТ2
М17
М18
М19 1/8 4 порт ОЛТ1
М20
М21 1/8 4 порт ОЛТ2
М22 1/8 2 порт ОЛТ1
Муфта Элката
КВУ
Ов8-126м
Ов8-200м
Ов12-112м
Ов12-95м
Ов12-197м
Ов8-218м
Ов8-146м
Ов8-160м
Ов8-210м
Ов8-136м
Ов8-124м
Ов2-132м
Ов8-147м
Ов2-104м
Ов8-207м
Ов8-340м
Ов8-330м
Ов8-392м
Ов8-364м
Ов8-400м
Ов8-318м
Ов8-338м
Ов8-357м
Ов2-150м
Ов2-157м
Ов2-105м
Ов2-215м
Ов2-213м
Ов2-214м
Ов2-104м
Ов2-125м
Ов2-75м
Ов2-310м
Ов2-388
Ов2-306м
Ов2-220м
Ов2-145м
Ов2-110м
Ов2-185м
Ов2-347м
Ов2-169м
Ов2-224м
Ов8-74м
Ов2-308м
Ов2-242м
Ов2-260м
Ов2-167м
Ов1-138м
Ов1-209м
Ов1-197м
Ов1-204м
Ов1-198м
Ов1-191м
Ов1-222м
Ов1-247м
Ов1-105м
Ов1-106м
Ов1-150м
Ов1-240м
Ов1-208м
Ов1-250м
Ов1-278м
Ов1-283м
Ов1-196м
Ов1-218м
Ов1-227м
Ов1-190м
Ов1-212м
Ов1-173м
Ов1-177м
Ов1-204м
Ов1-194м
Ов1-188м
Ов1-158м
А1
А2
А3
А4
А5
А6
А7
А8
А9
А10
А11
А12
А13
А14
А15
А16
А17
А18
А19
А20
А21
А22
А23
А24
А25
А26
А27
А28
А29
А30
А31
А32
А33
А34
А35
А36
А37
А38
А39
А40
А41
А42
А43
А44
А45
А46
А47
А48
А49
А50
А51
А52
А53
А54
А55
А56
А57
А58
А59
А60
А61
А62
А63
А64
А65
А66
А67
А68
А69
А70
А71
А72
А73
А74
А75
А76
А77
А78
А79
А80
А81
А82
А83
А84
А85
А86
557/1
Ф4 тп 2867 На какое нет доступа